
PLAN (scale 1:50)

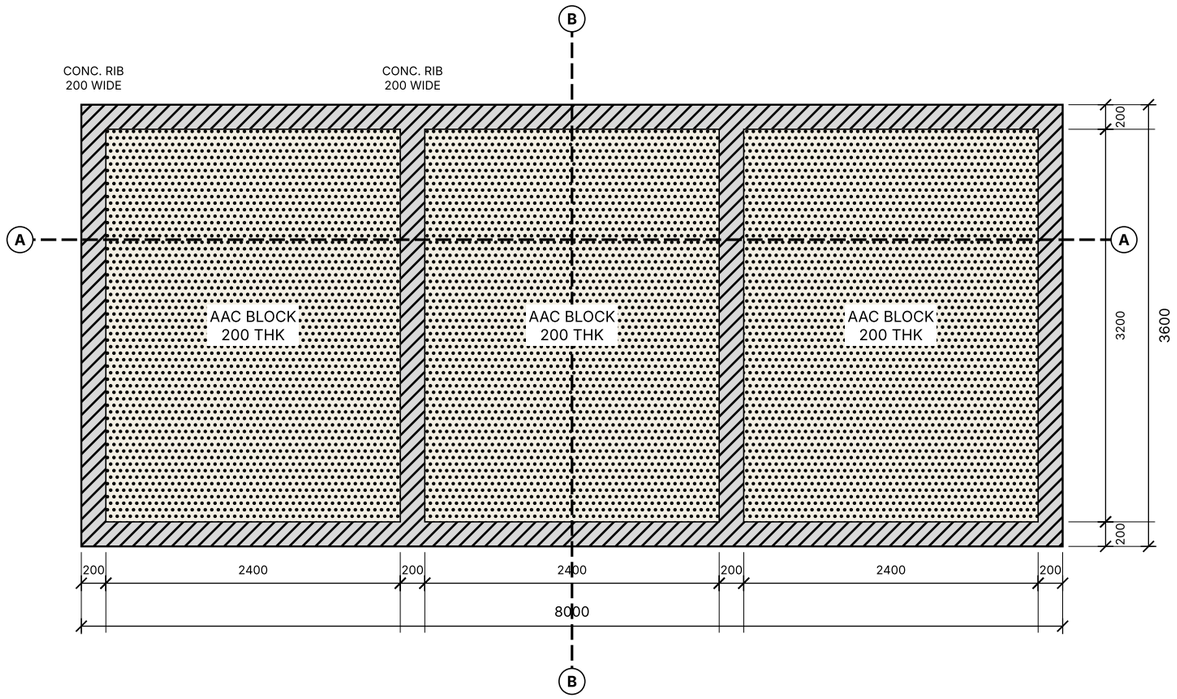


LEGEND

- Reinforced concrete (ribs / topping slab)
- AAC block infill, 200 mm thick
- Existing roof slab (reference)
- 6 mm BRC mesh


NOTES

1. All dimensions are in mm unless noted otherwise.
2. Overall upstand size 8000 x 3600 mm, total height 350 mm above existing roof slab.
3. Concrete ribs 200 mm wide x 200 mm high along the full perimeter and at two intermediate positions (3 equal bays of 2400 mm clear), cast on the roof slab.
4. AAC block infill, 200 mm thick, laid in the three bays between the ribs.
5. RC topping slab 150 mm thick over the full area, reinforced with one layer of 6 mm BRC mesh placed at mid-depth, continuous over the ribs.
6. Mesh spacing and concrete grade: TO BE CONFIRMED by the engineer.
7. Existing roof slab shown for reference only; verify its capacity for the tank load.


SECTION A-A (scale 1:50)

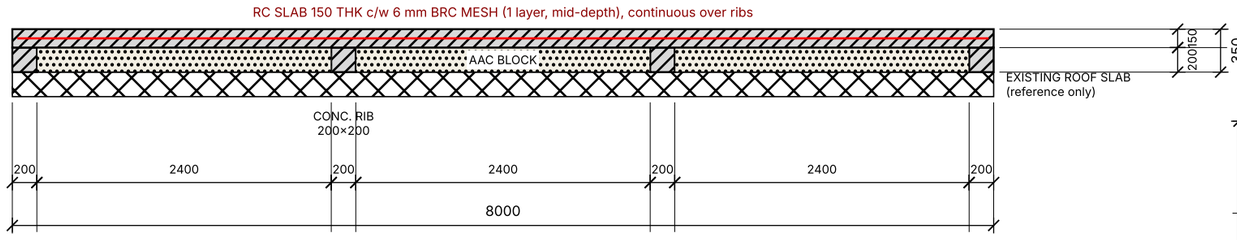

SECTION B-B (scale 1:25)

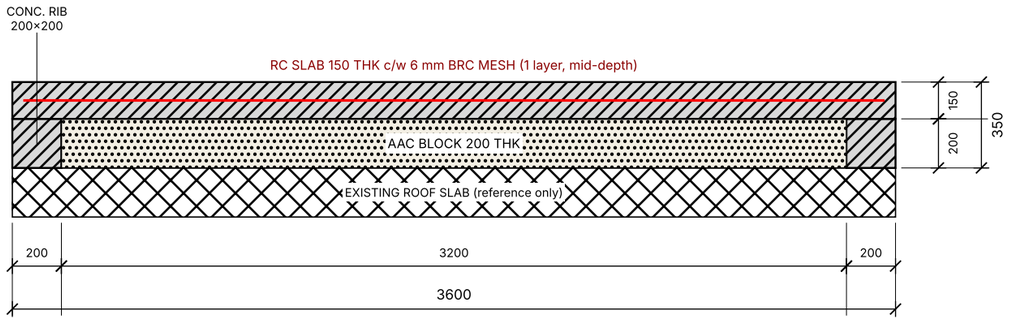

TYPICAL EDGE DETAIL (scale 1:10)

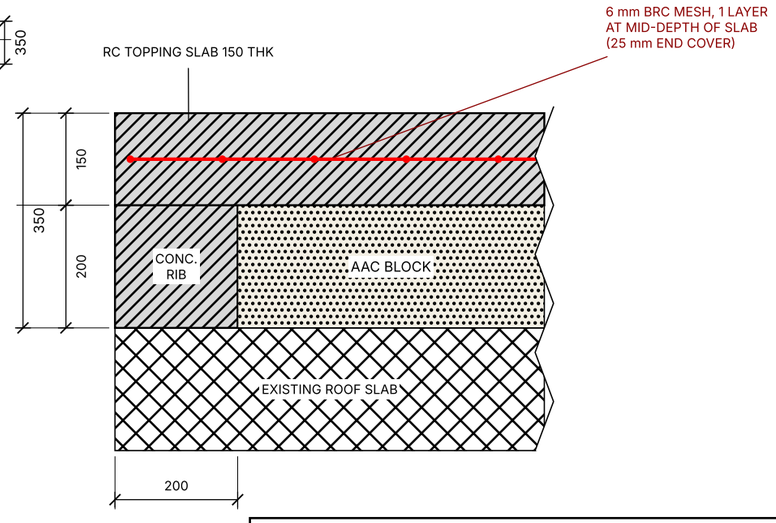

WATER TANK UPSTAND ON ROOF - PLAN, SECTIONS & DETAIL	
SCALES: AS NOTED @ A3	UNITS: mm
DATE: 2026-10-24	DWG No: WT-UPS-01 REV: 0