

PLAN (scale 1:50)

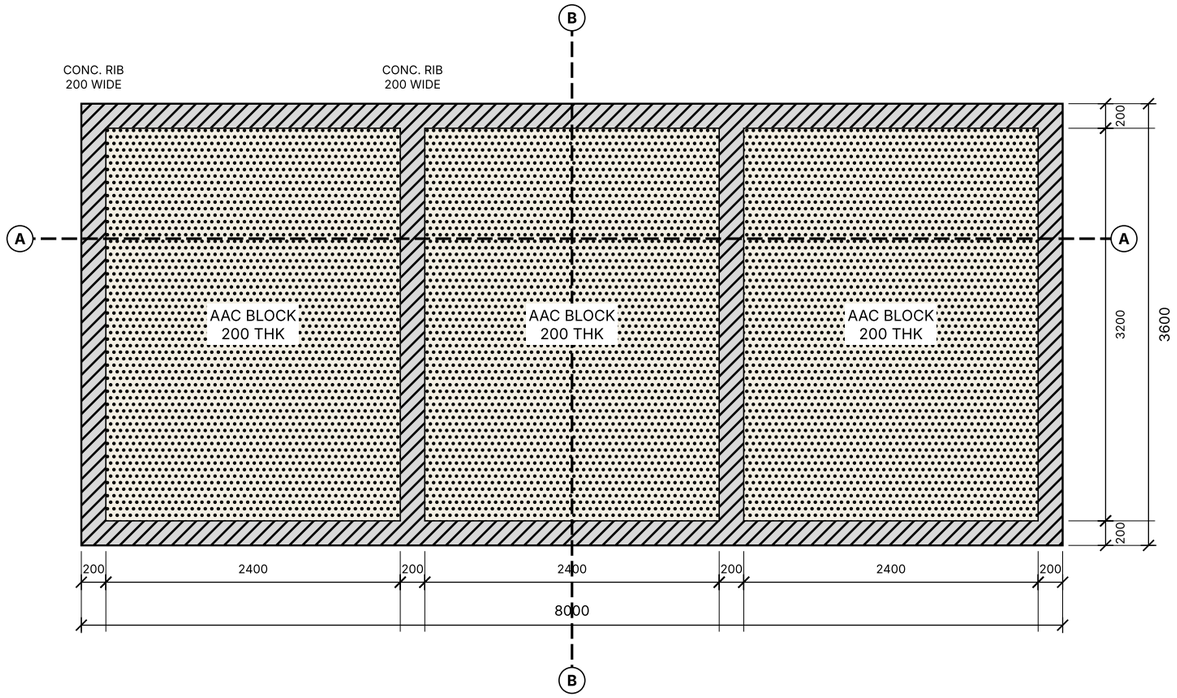


LEGEND

- Reinforced concrete (ribs / topping slab)
- AAC block infill, 200 mm thick
- Existing roof slab (reference)
- 6 mm BRC mesh


SECTION A-A (scale 1:50)

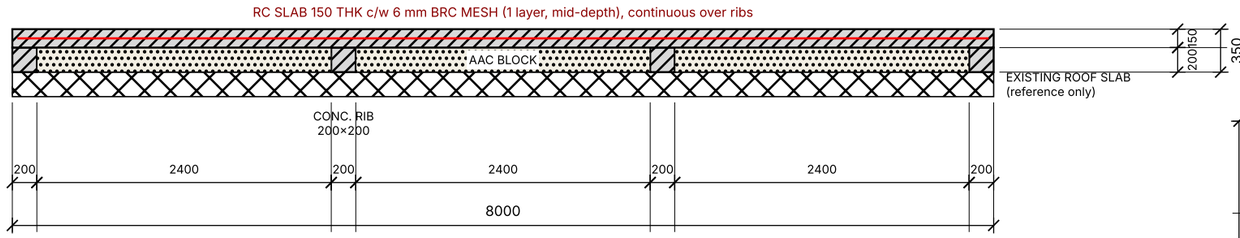

SECTION B-B (scale 1:25)

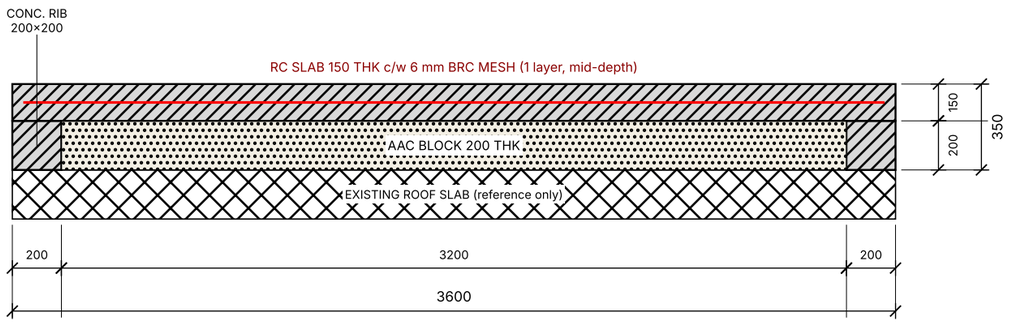

TYPICAL EDGE DETAIL (scale 1:10)

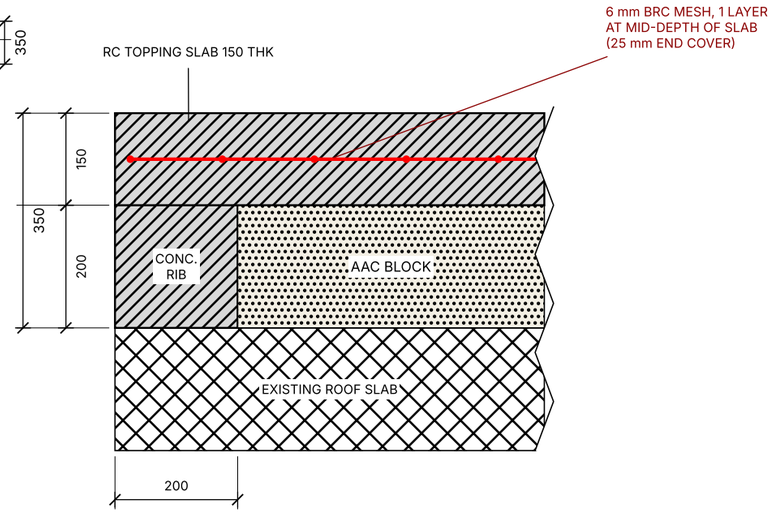

WATER TANK UPSTAND ON ROOF - PLAN, SECTIONS & DETAIL	
SCALES: AS NOTED @ A3	UNITS: mm
DATE: 2026-10-24	DWG No: WT-UPS-01 REV: 0